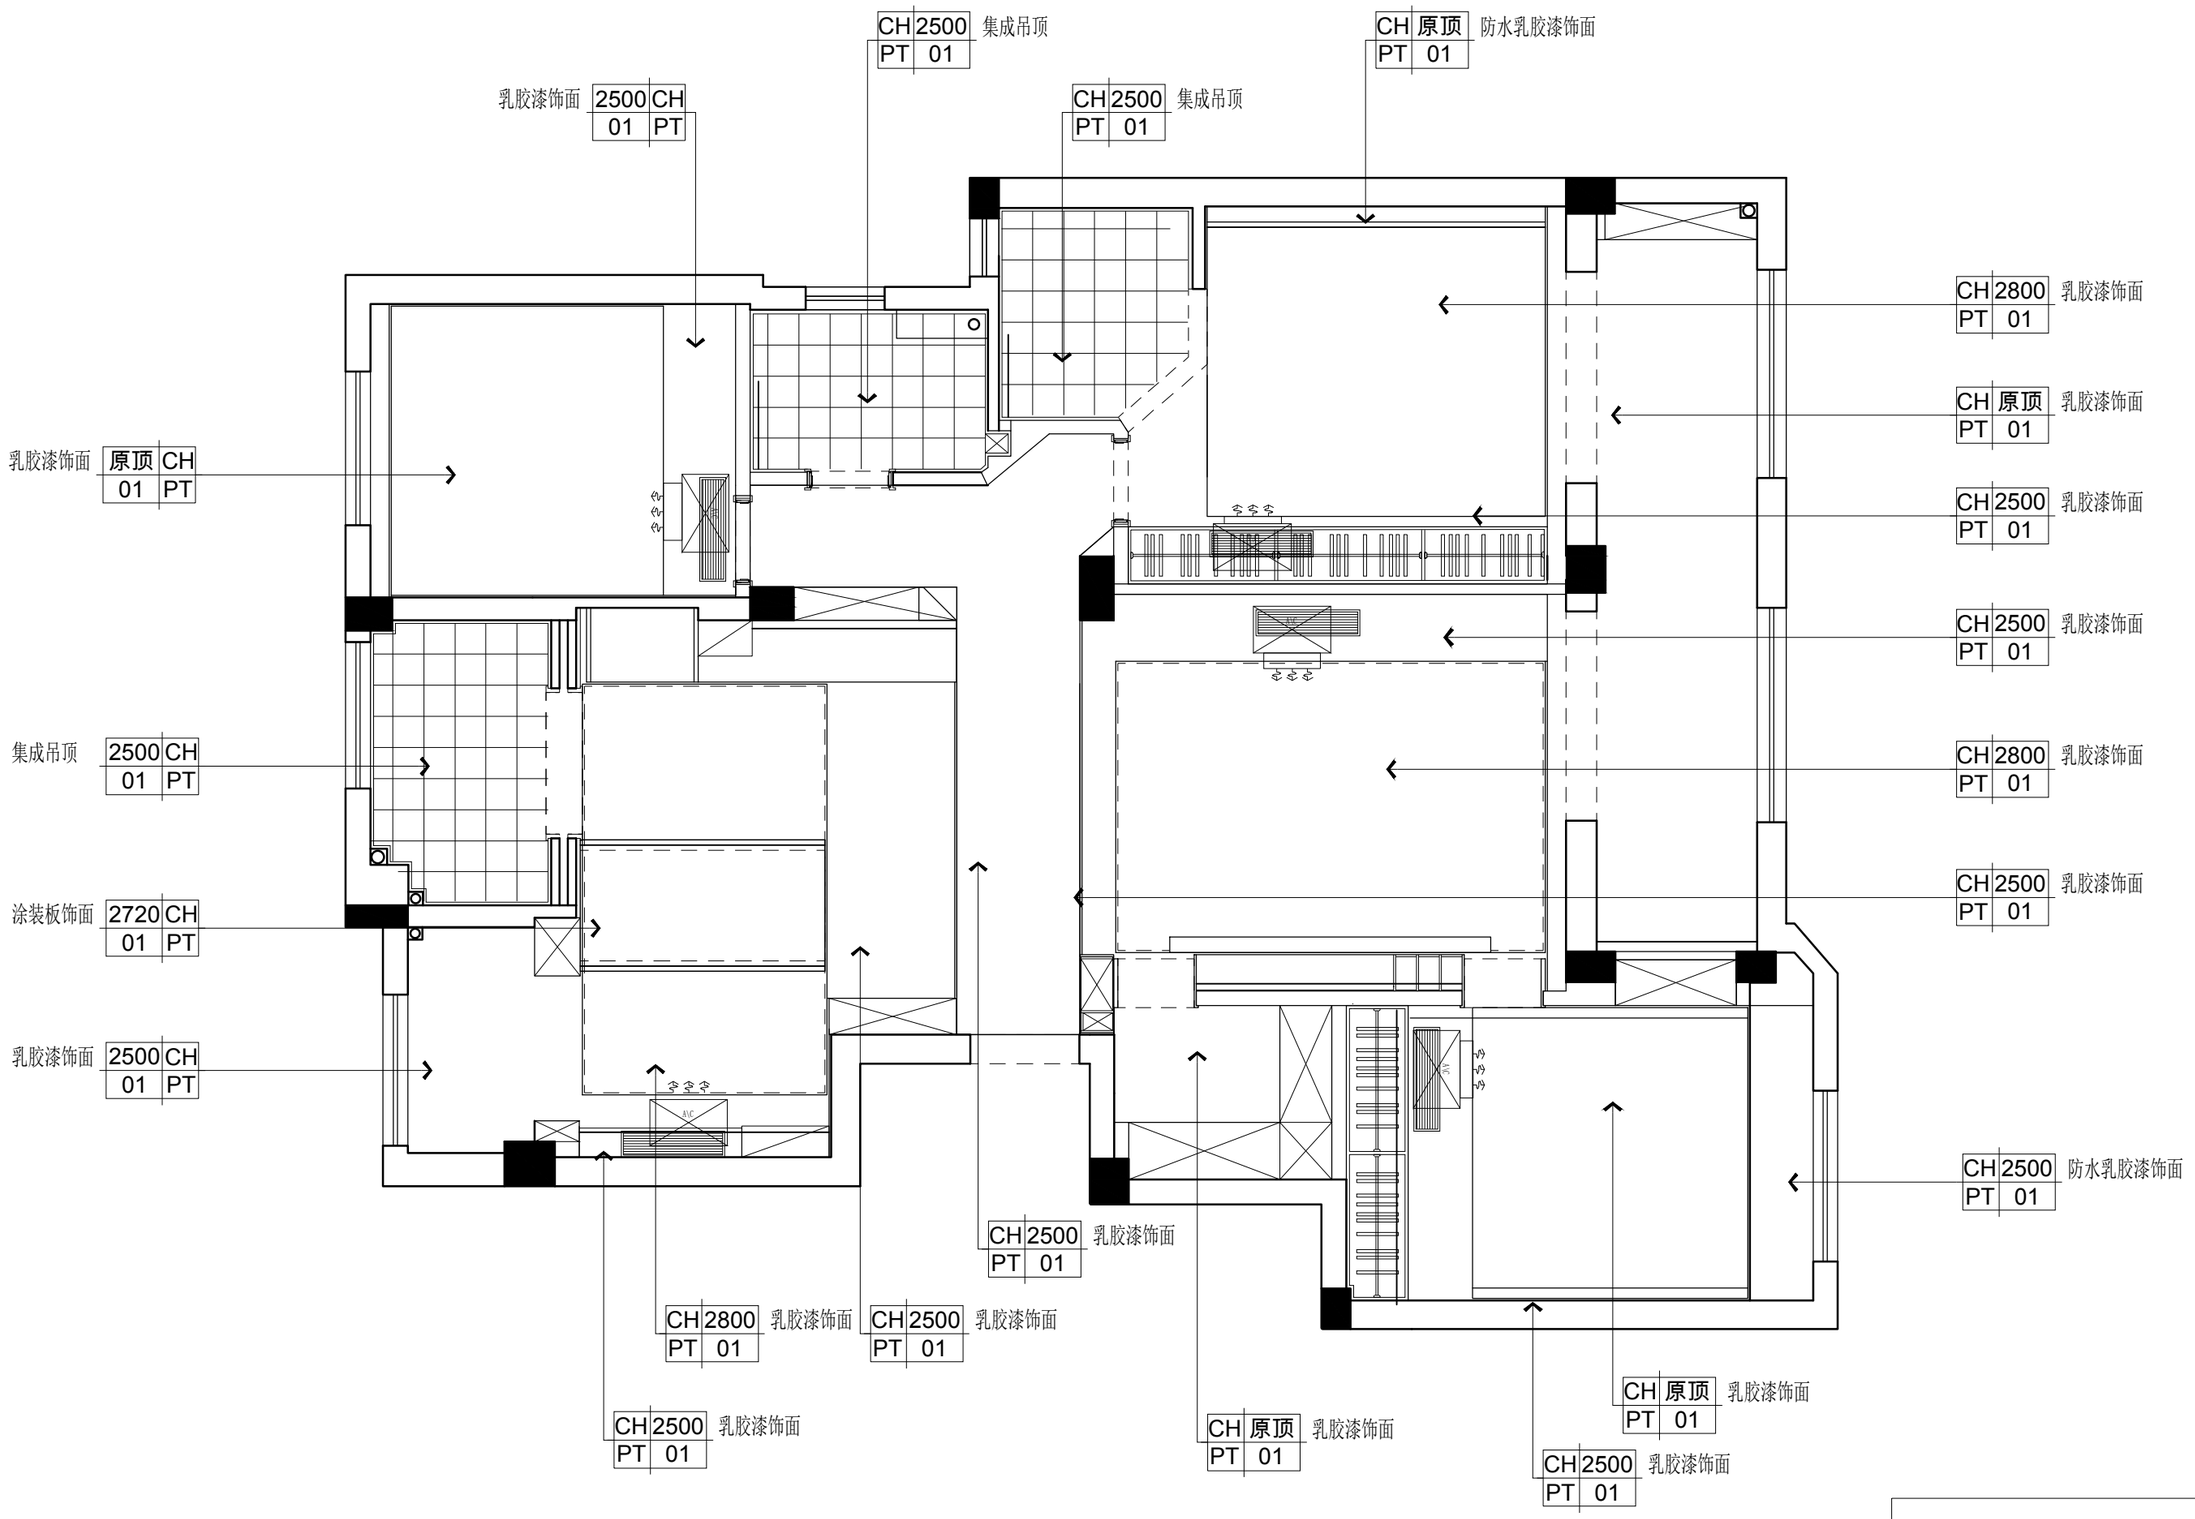

注：本图天花标高为距地面完成面尺寸

RC REFLECTED CEILING PLAN 天花造型尺寸及空调设备定位图